

ESTOS PLANOS NO SON VÁLIDOS PARA FABRICACIÓN HASTA SU REVISIÓN Y APROBACIÓN POR UN INGENIERO CALCULISTA HABILITADO.

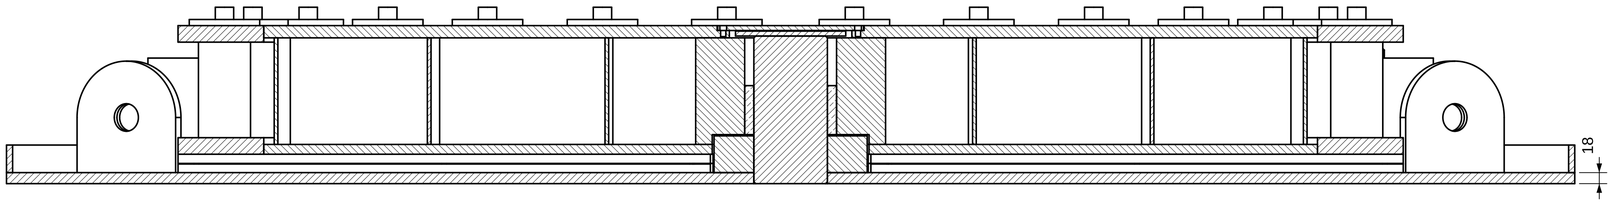


CORTE B-B (plano x = 0)

ESC 1:5

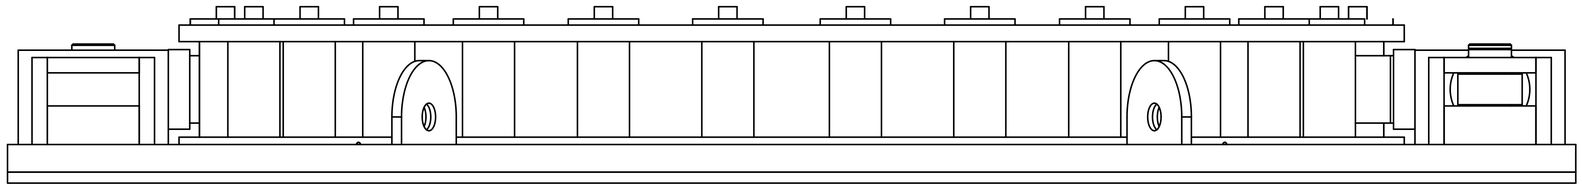


ELEVACIÓN FRONTAL (cotas de altura en CON-001, corte A-A)

ESC 1:5

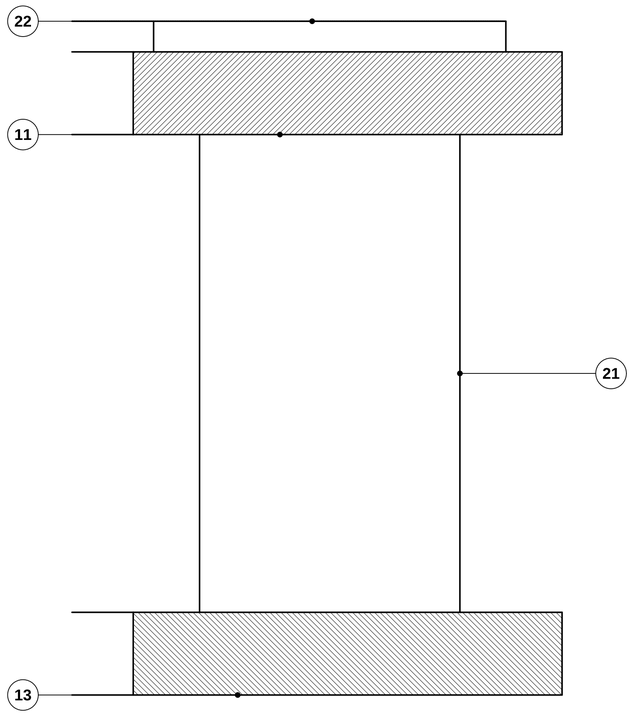

DETALLE A: PASADOR, ARANDELA Y PERNO EN EL BORDE DE LA MESA

ESC 1:1

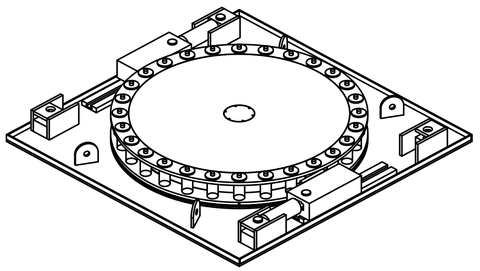

VISTA ISOMÉTRICA

SIN ESCALA (referencial, no medir)

NOTAS

Cotas de instalación, centro de gravedad, huella y holguras: CON-001.
Dimensiones de fabricación: planos de cada pieza.
En caso de vientos fuertes no se recomienda realizar la operación.

Equipo sin anclaje: apoyo sobre losa/mats con presión sobre la losa ≤ 2 MPa (admisible del cálculo); verificar la superficie de apoyo por terceros.

Tolerancias generales ISO 2768-mK; soldadura ISO 2553 / ISO 5817; rugosidad ISO 1302; GD&T ISO 1101. Cotas en mm salvo indicación. No medir sobre el plano. Proyección: método E (primer diedro).

REV	FECHA	DESCRIPCIÓN	DIB.	REV.	APR.
C	07-11-2026	EMITIDO PARA REVISIÓN. Juego de planos de fabricación rehecho: conjunto, subconjuntos, piezas, soldaduras ISO 2553, ajustes ISO 286, inspección y listas. Valores leídos del JSON de diseño del núcleo.	A DEFINIR	A DEFINIR	A DEFINIR
B	—	Emisión anterior (planos básicos), reemplazada por la rev. C.	—	—	—

EMITIDO PARA REVISIÓN — NO APTO PARA FABRICACIÓN HASTA SU APROBACIÓN

PROYECTO
TT300-C · TORNAMESA HIDRÁULICA 300 tf
Interfaz: Opción C-1: placa de bronce con tapones de grafito + disco duro

TÍTULO
CONJUNTO GENERAL: CORTE B-B, ELEVACIÓN FRONTAL Y DETALLE DEL PASADOR

MATERIAL	MASA	TRATAMIENTO
Ver despiece	3.904,3 kg (conjunto)	Ver notas

DIBUJÓ	REVISÓ	APROBÓ
A DEFINIR	A DEFINIR	A DEFINIR
firma / fecha	firma / fecha	firma / fecha

ESCALA	FECHA	FORMATO	MÉTODO DE PROYECCIÓN
1:1 / 1:5	07-11-2026	A1 (841×594)	E

PLANO N°	LÁMINA	REV.
TT300C-CON-003-C	4 de 64	C